



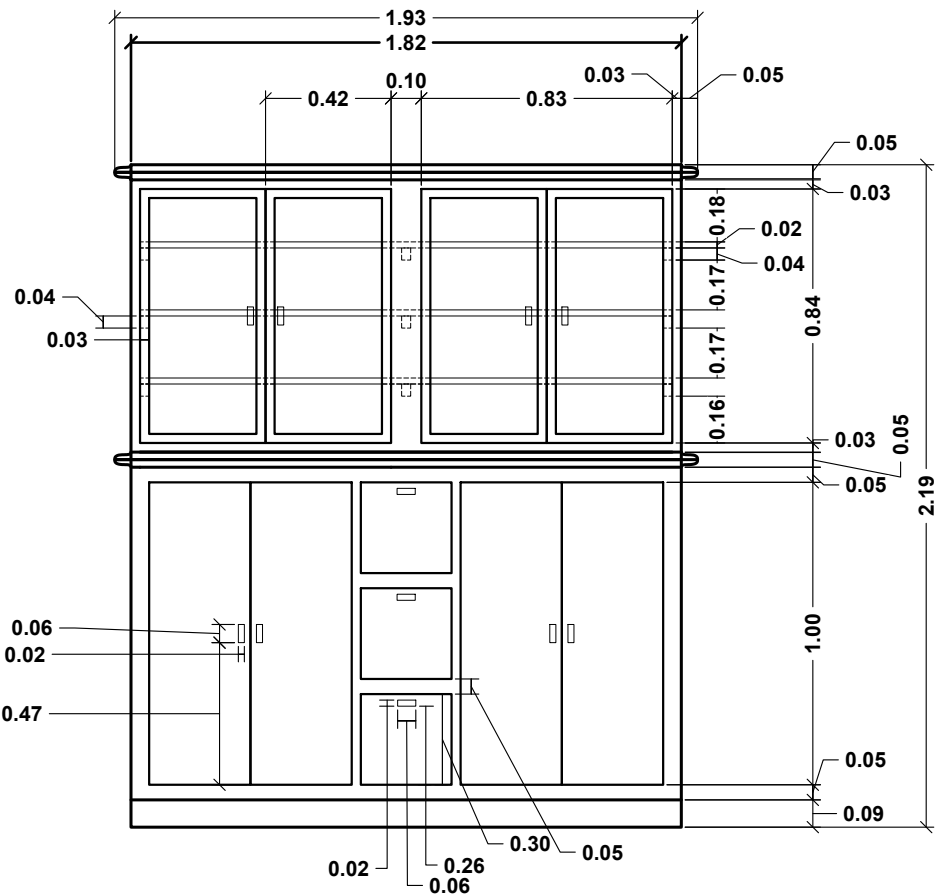


A1

VISTA FRONTAL
ESCALA 1:25

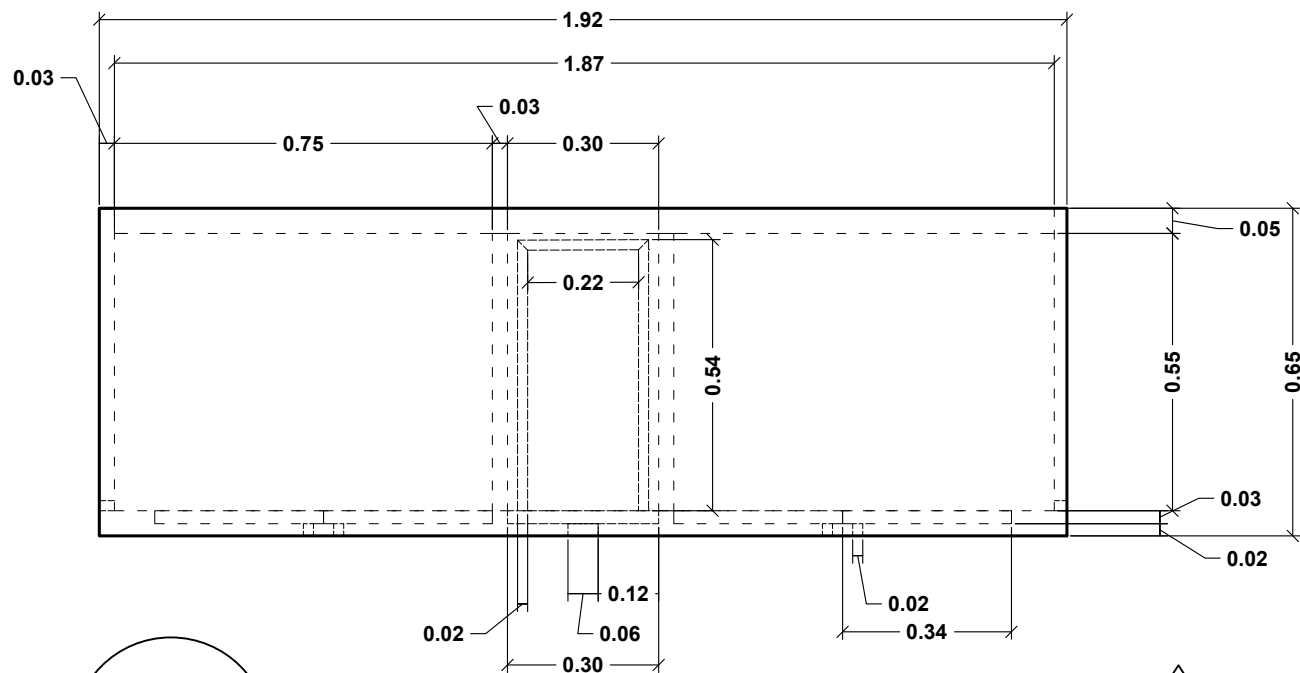

D1

VISTA EN PLANTA
ESCALA 1:15

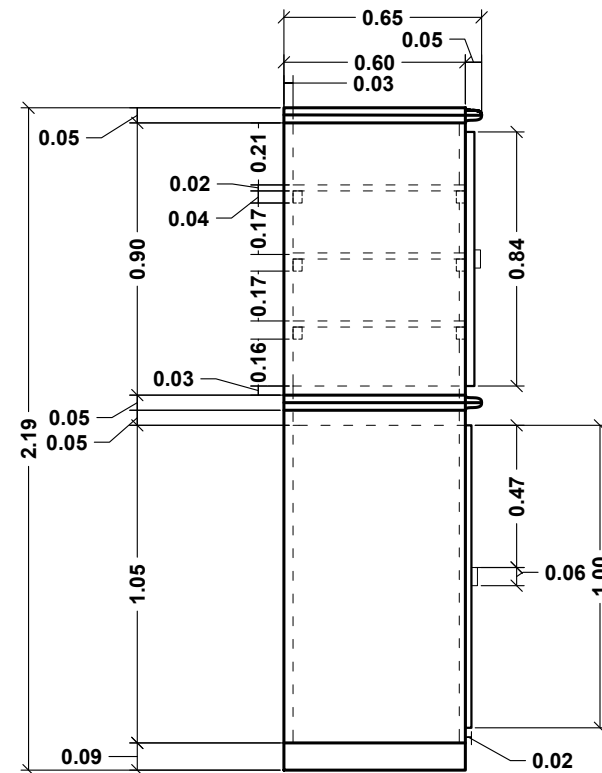

A5

VISTA LATERAL
ESCALA 1:25

	PROPIETARIO:		PLANO:	
	ISAI MIRANDA		1 / ISO 5457 - ISO 7200	
	PROYECTO:		FECHA:	No. Lámina:
			6/09/2026	
	PROYECTO INDEPENDIENTE		DIBUJADO:	
			ISAI MIRANDA	
			Unidades:	A3
			METERS	